



# Portfólio 2025

*Projetos Autorais  
Acadêmicos*

Por: Débora Maria Andrade Carvalho


# Sumário



Casa Raiz



Apartamento  
Efetivo

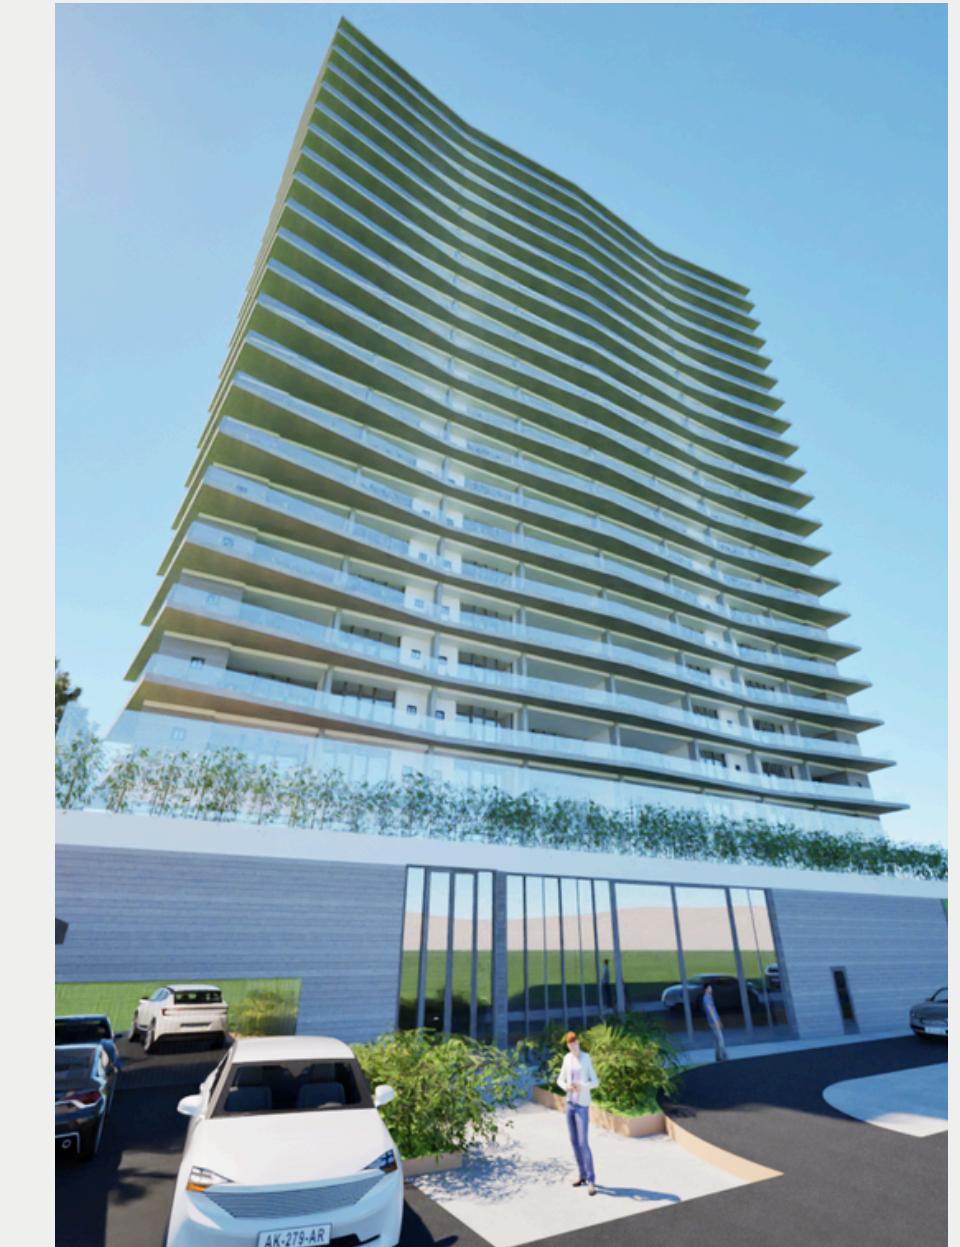

Edifício  
Orgânico




Fachada

# Casa Raiz

A residência combina elementos tradicionais e contemporâneos, com telhado cerâmico, volumes geométricos e materiais como concreto, madeira e vidro. A fachada horizontalizada destaca-se pelo paisagismo integrado e amplas aberturas, garantindo iluminação e ventilação naturais. O projeto prioriza fluidez e setorização funcional, criando um ambiente sofisticado e acolhedor, ao mesmo tempo, integrando a habitação pessoal à área comercial.


Programa: Archicad  
Render: Twinmotion

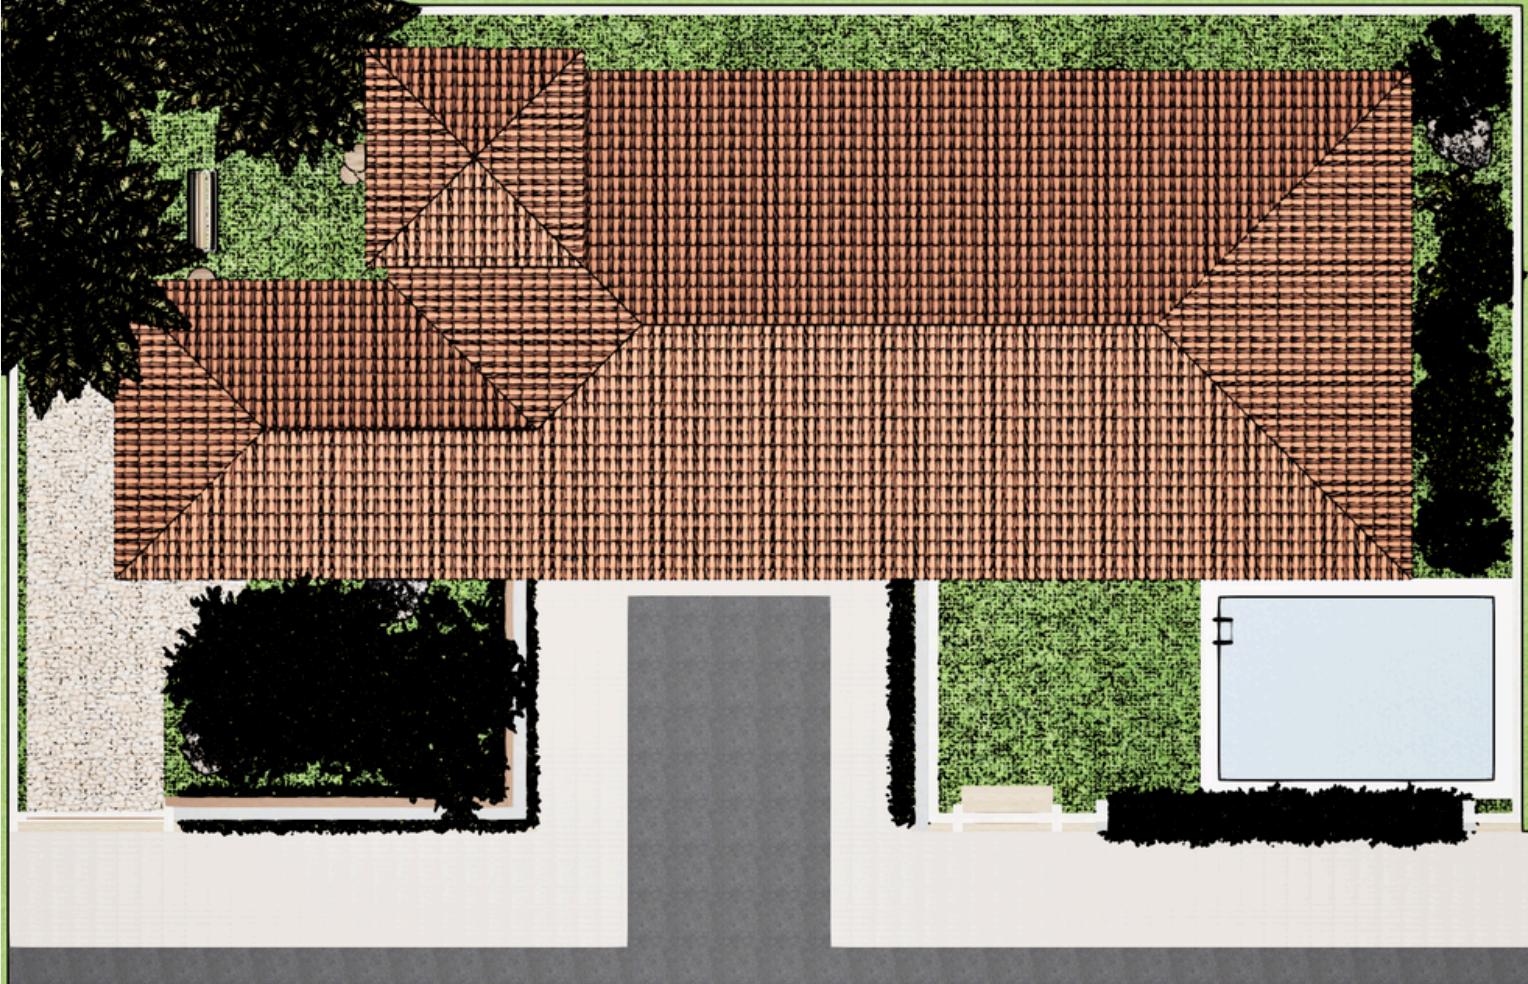







FACHADA

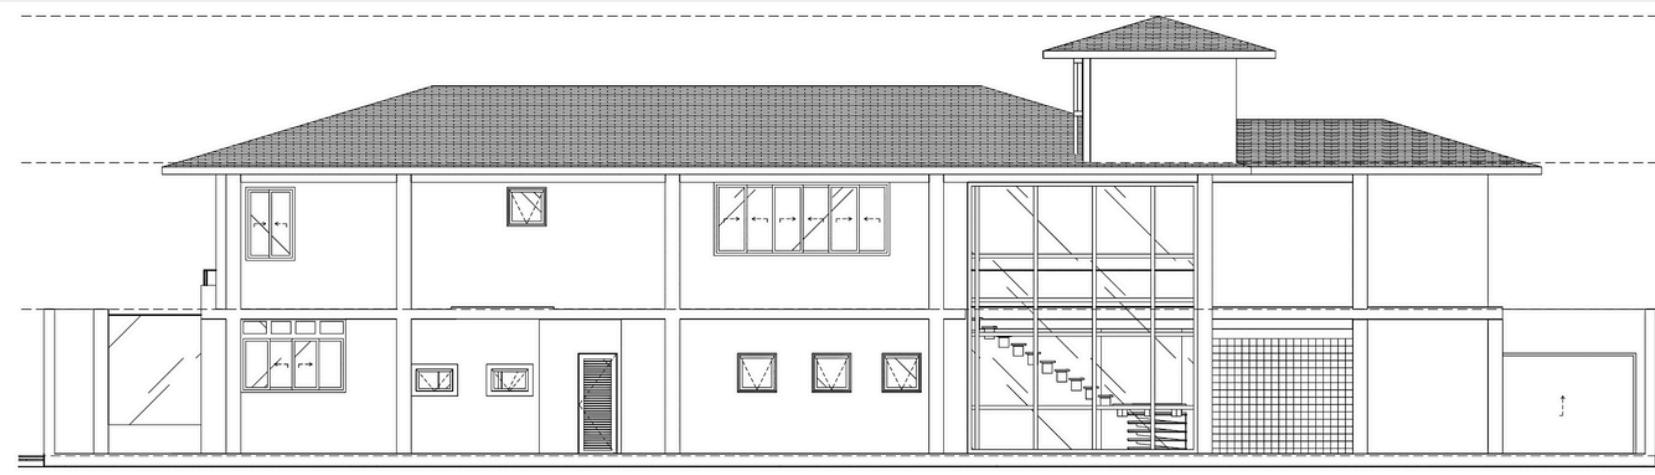

FACHADA - POSTERIOR

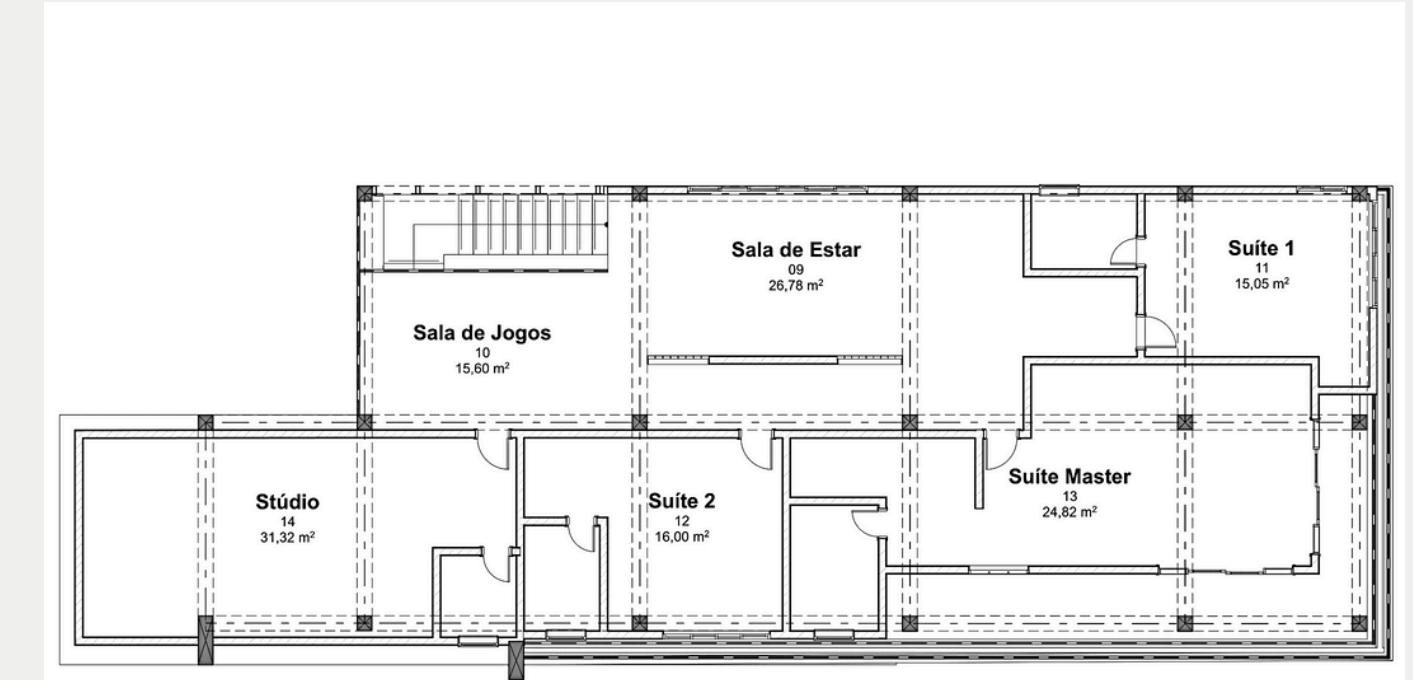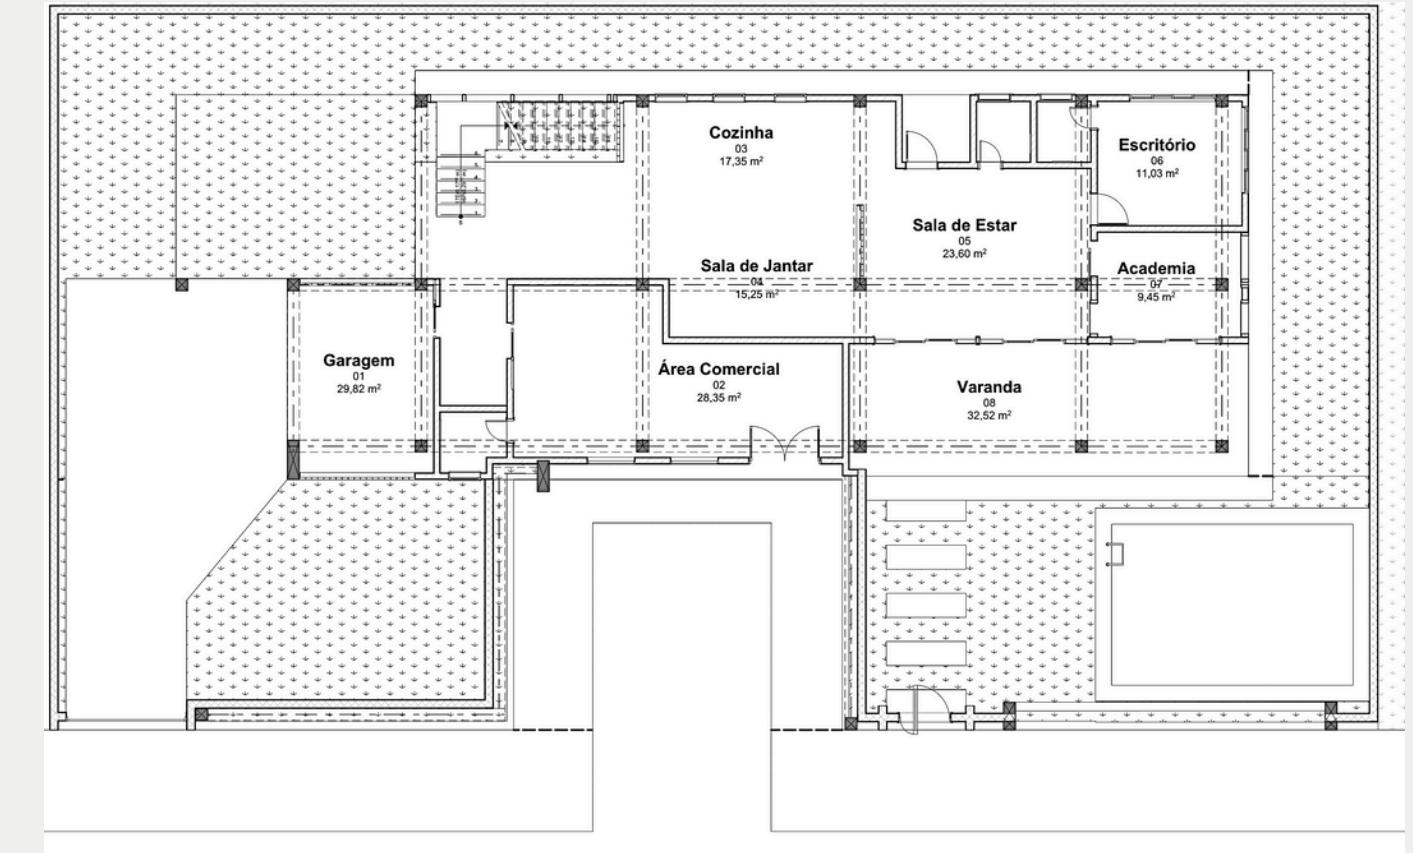


PLANTA BAIXA - PAV. SUPERIOR


# Apartamento Afetivo

O design de interiores do apartamento reflete a história e a memória afetiva dos moradores, unindo estética boho/rústica, conforto e conexão com a natureza. A proposta busca integrar elementos do passado a um espaço funcional e adaptado à vida urbana, criando um lar acolhedor que equilibra modernidade e tradição.


Programa: AutoCAD / SketchUp / SketchUp Layout

Render: Enscape

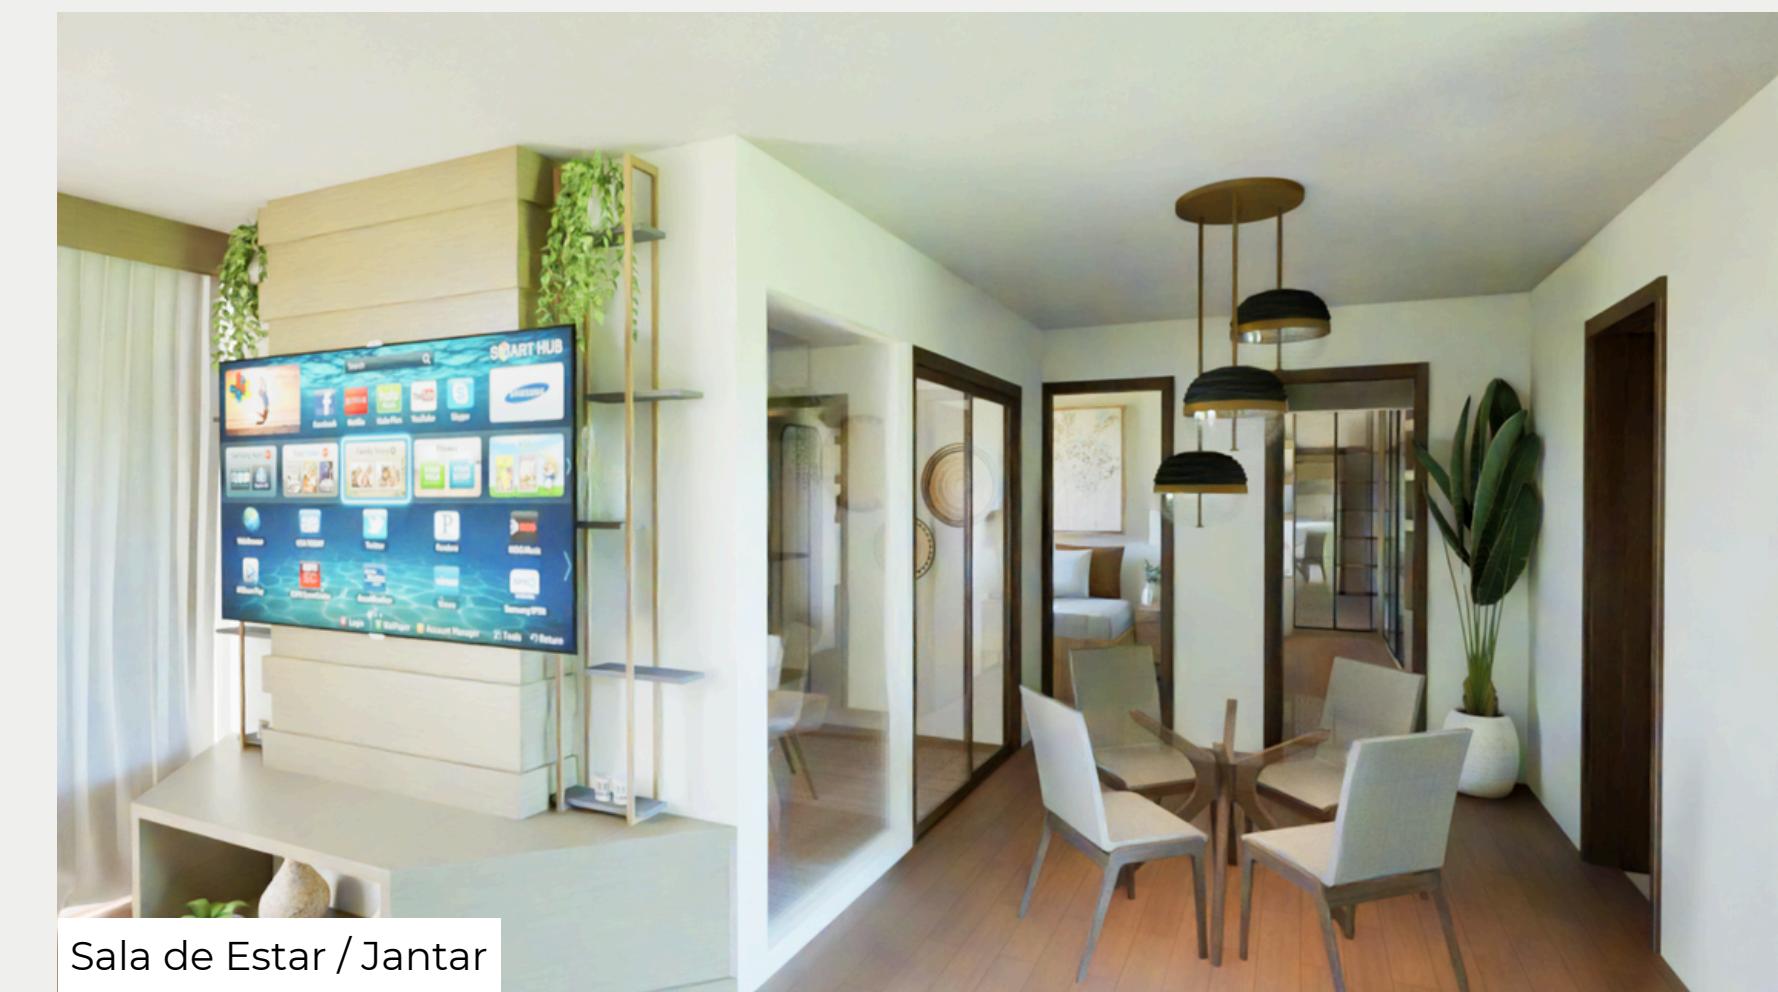


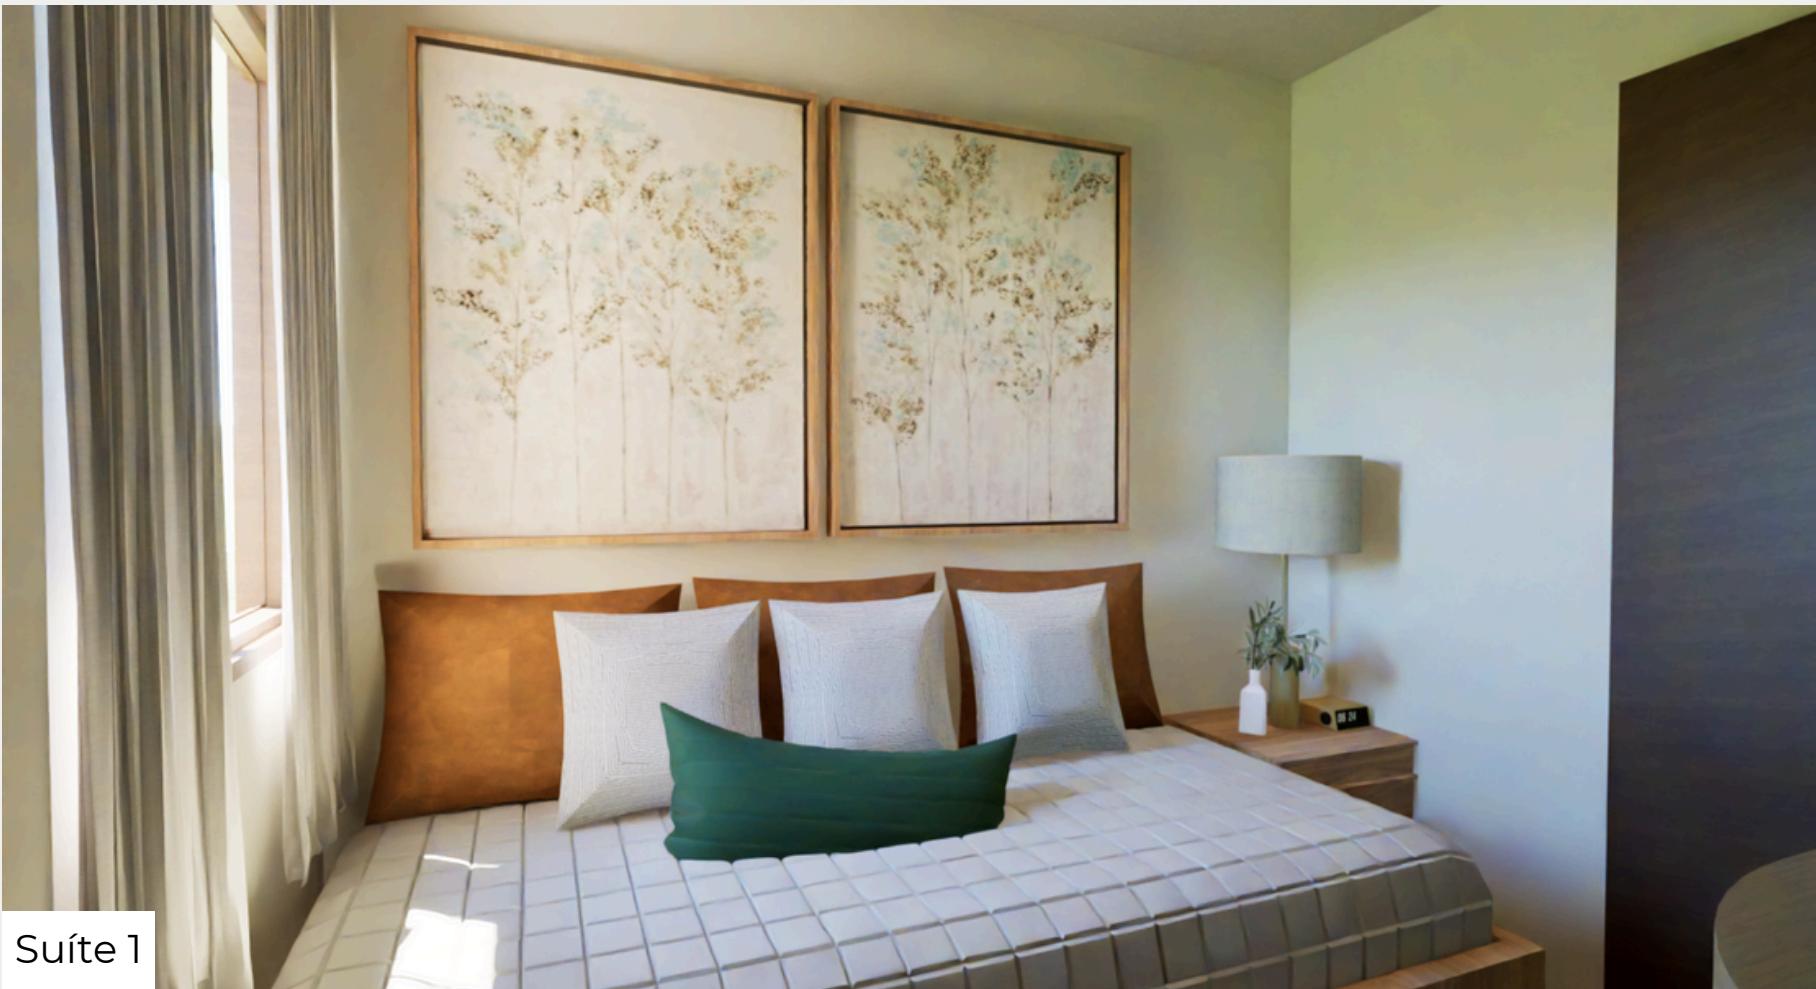


Suíte 1

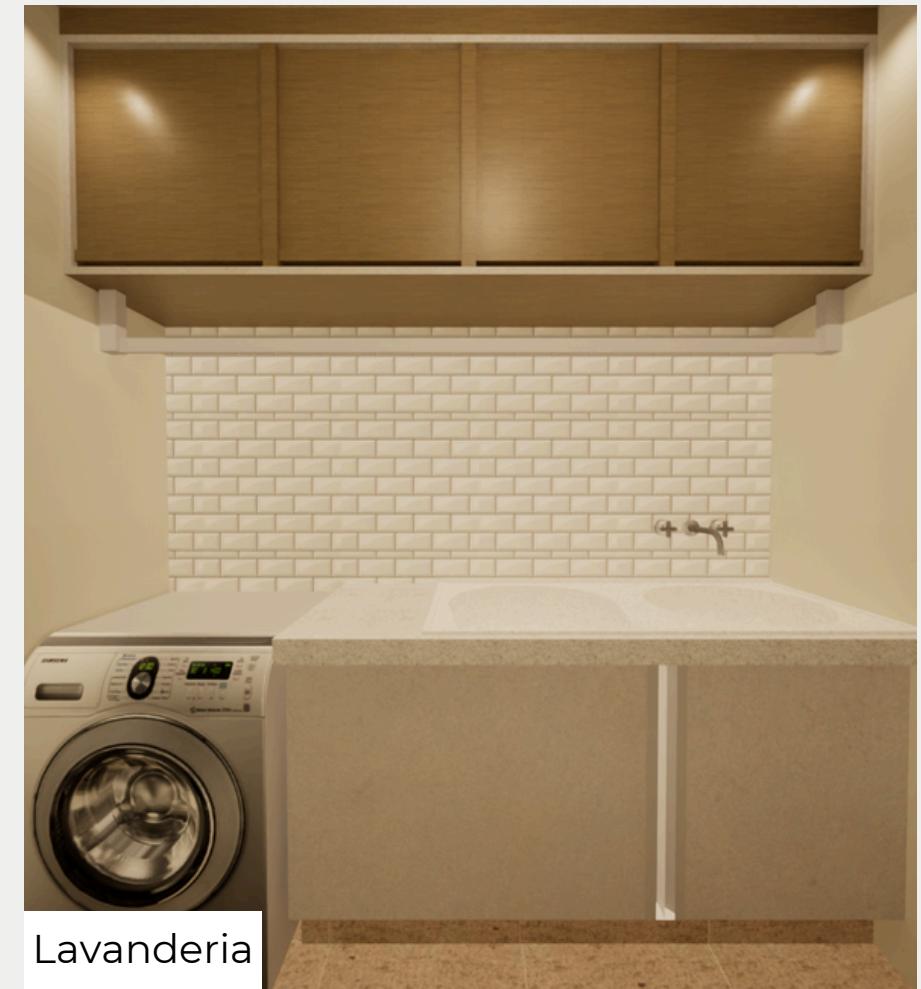

Lavanderia

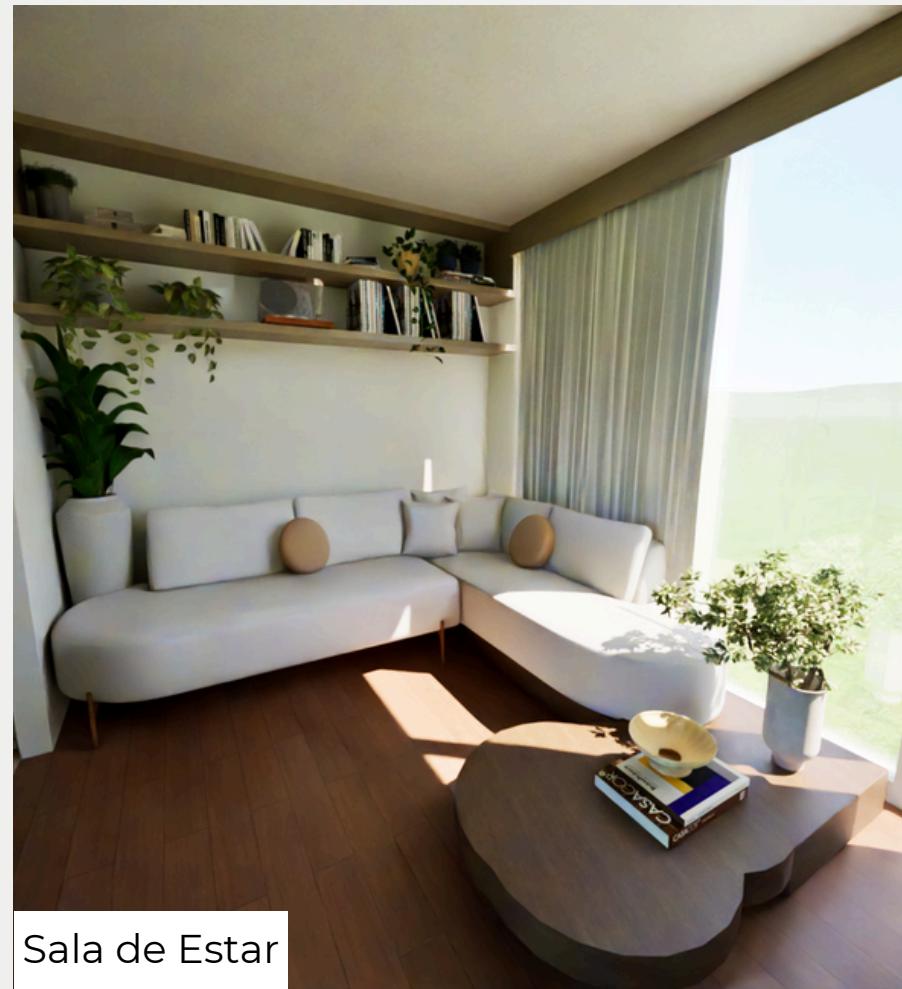

Sala de Estar

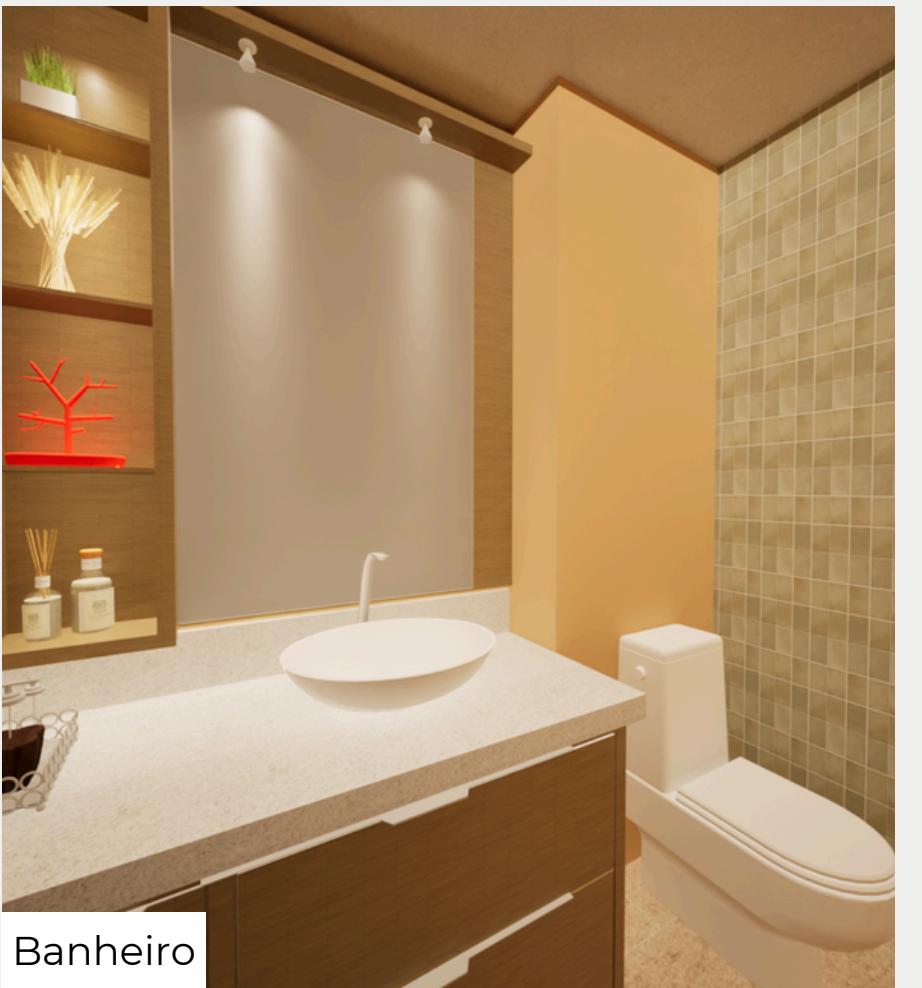





Banheiro



Ateliê



Suíte Master

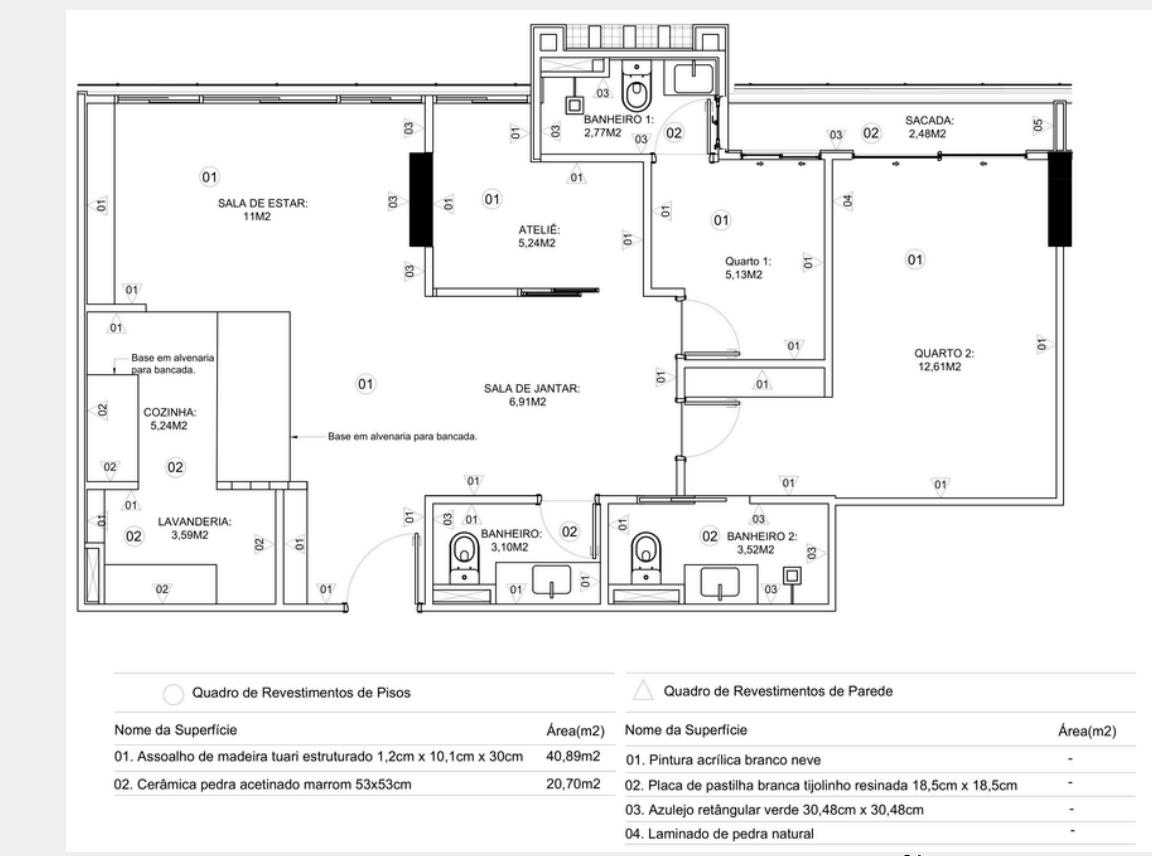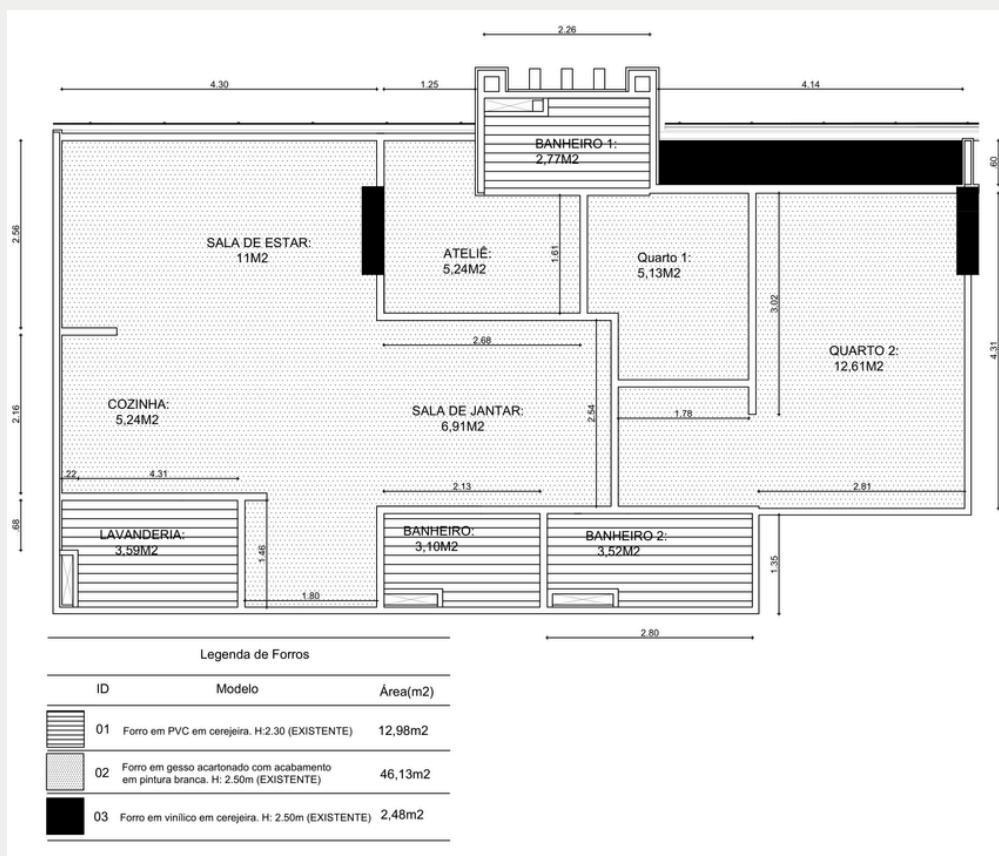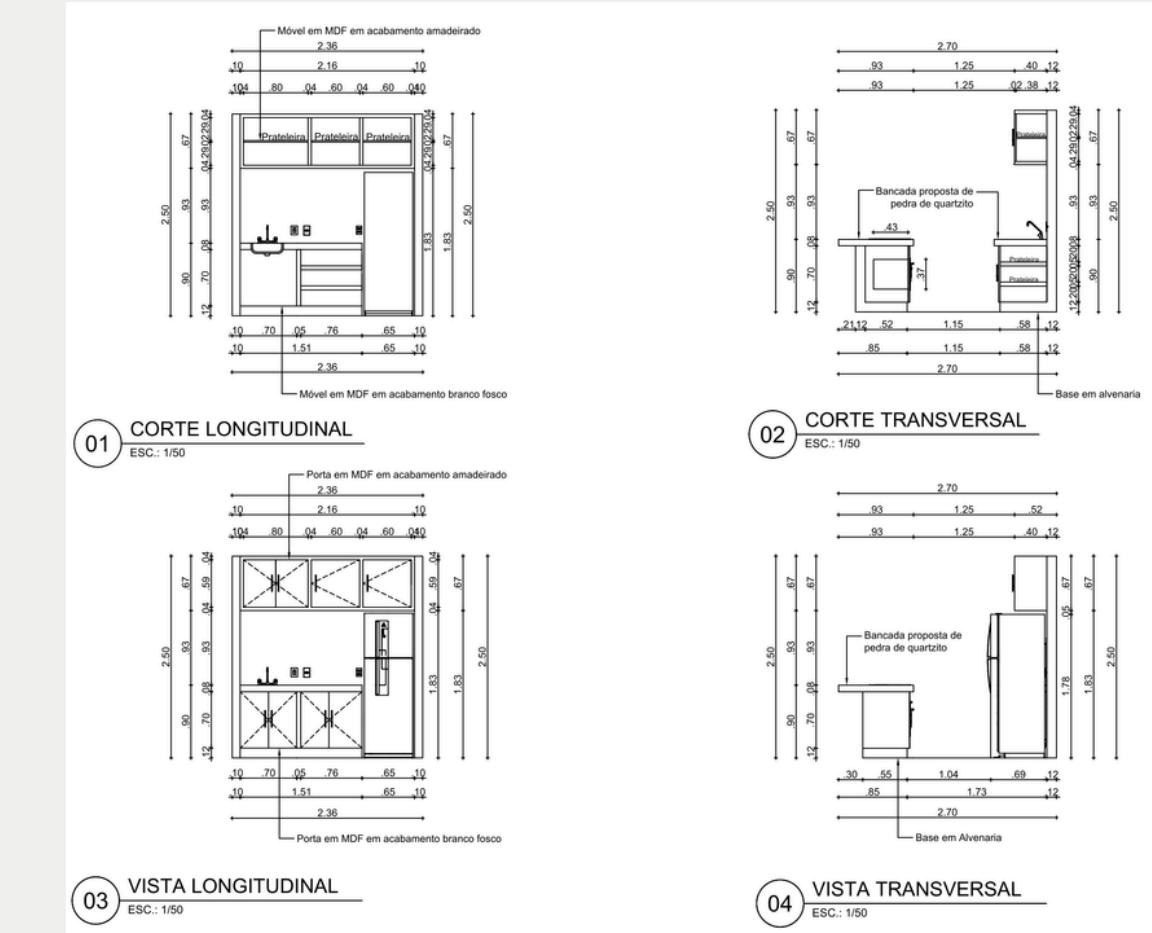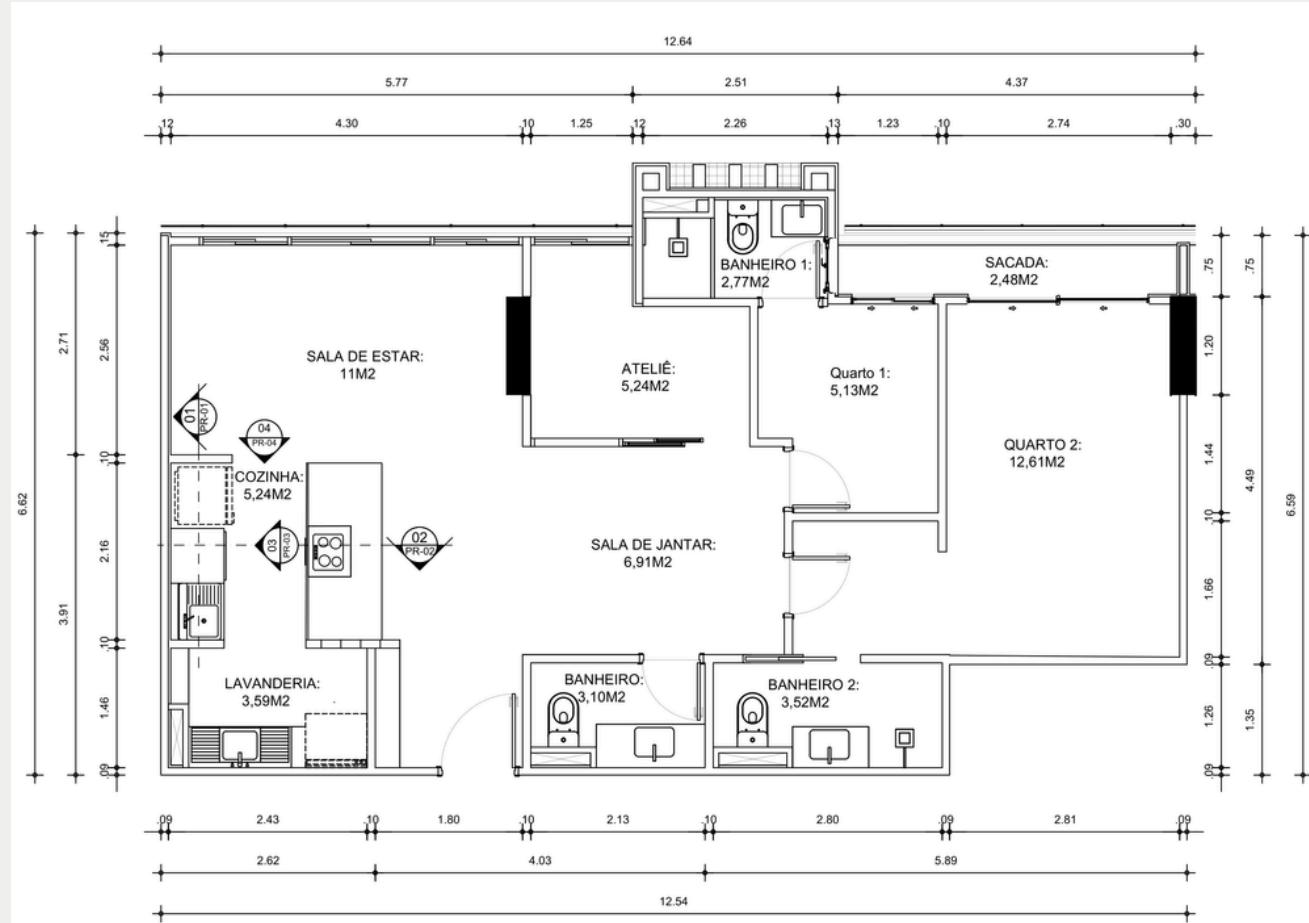

# Edifício Orgânico

O edifício de 20 pavimentos, integra vida urbana e natureza com uma base aberta conectada ao entorno, ao mesmo tempo, integrando o prédio residencial à áreas comerciais no térreo. Formas orgânicas e jardineiras na fachada, pilotis e pavimento superior equilibram a robustez do concreto com a leveza da vegetação.


Programa: Archicad

Render: Twinmotion




Fachada




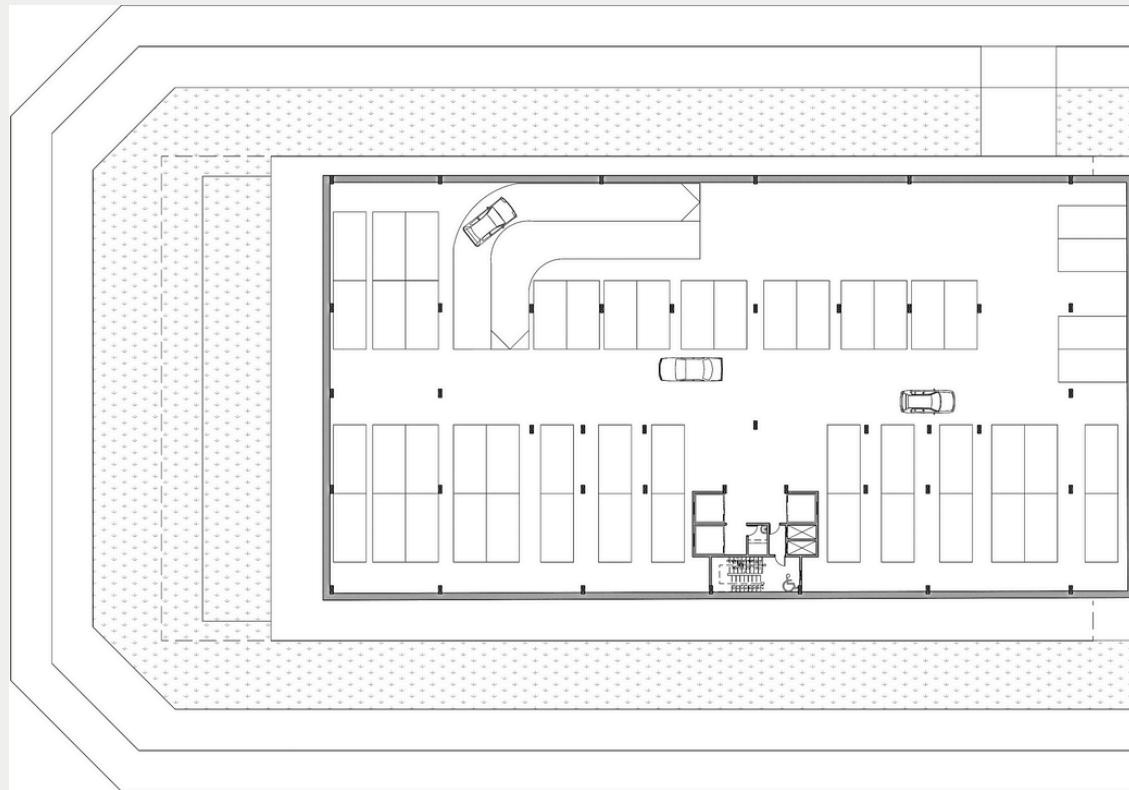


PLANTA BAIXA DE SUBSOLO

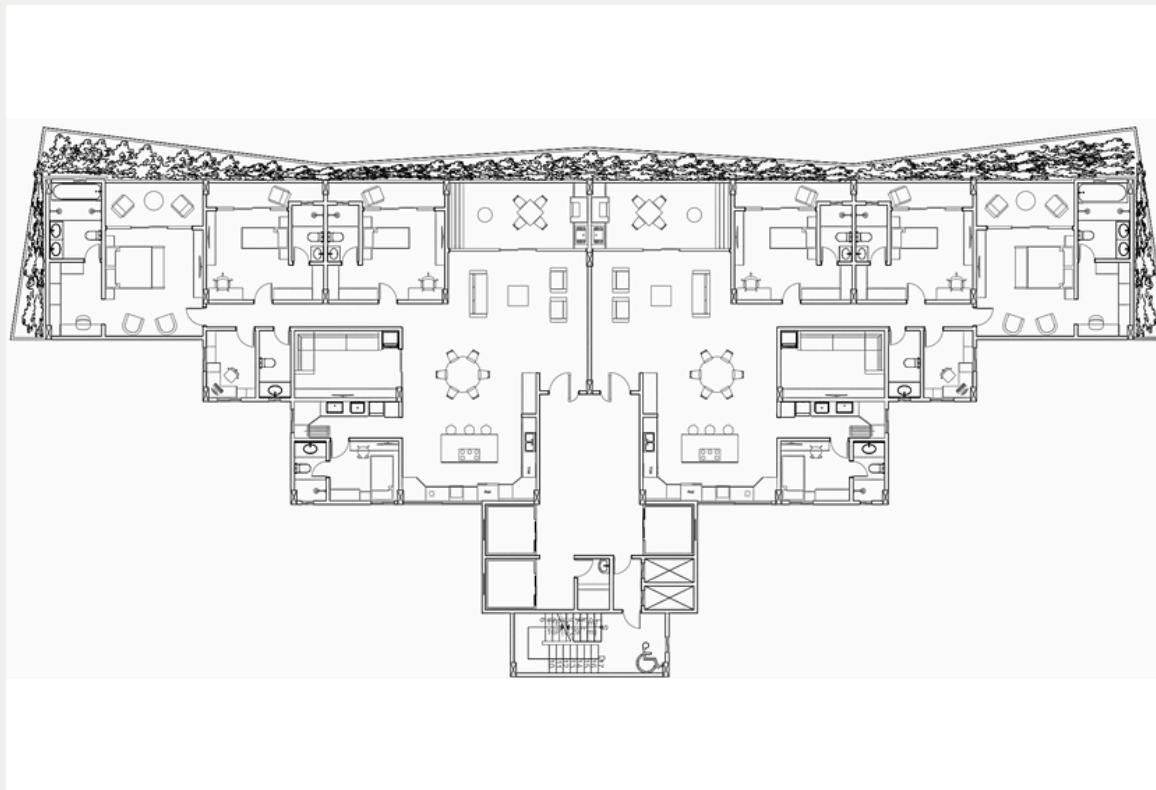


PLANTA BAIXA - PAV. TIPO

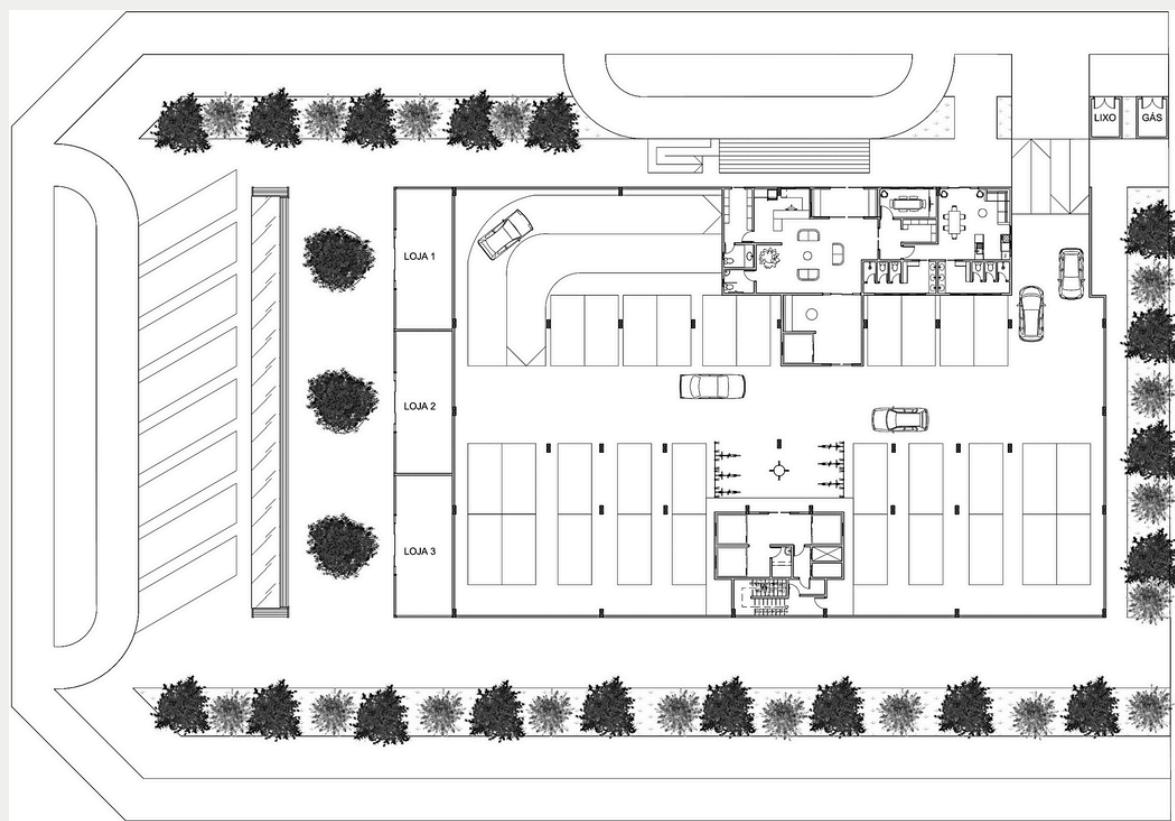

PLANTA BAIXA - PILOTIS(TÉRREO)

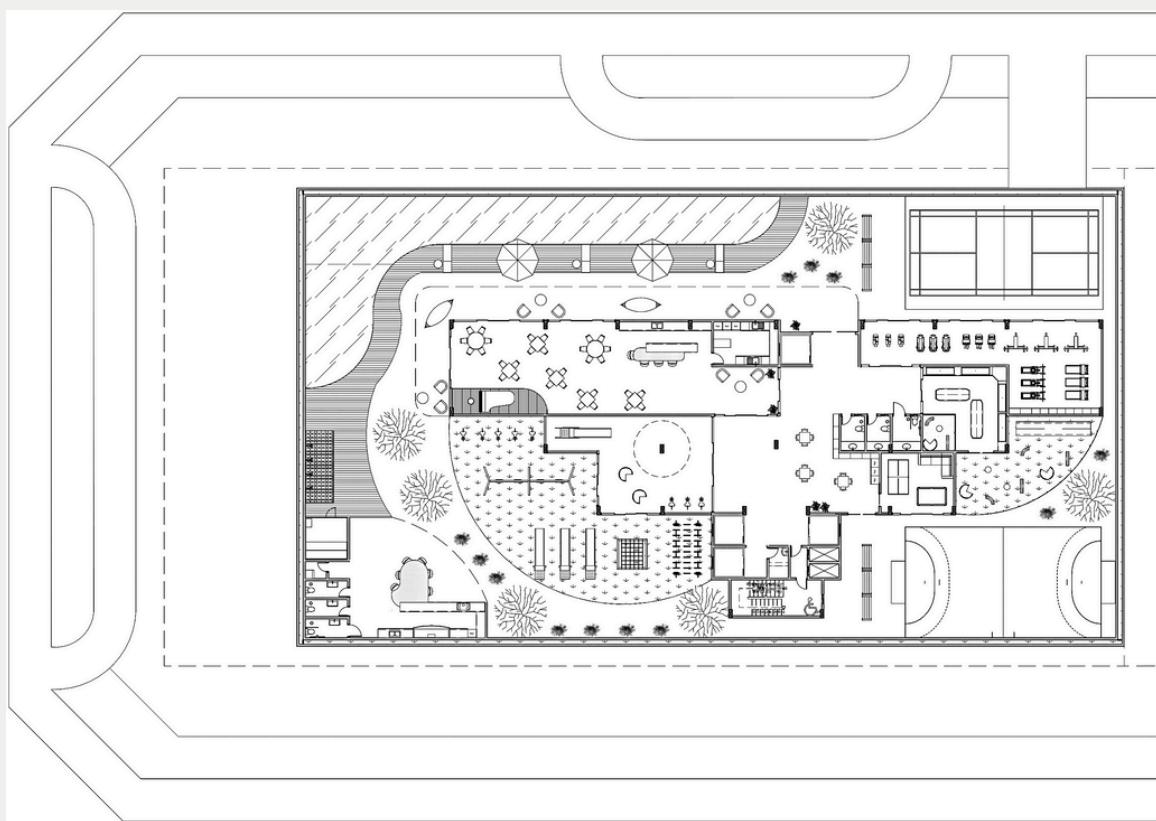

PLANTA BAIXA - PILOTIS(PAV. SUPERIOR)

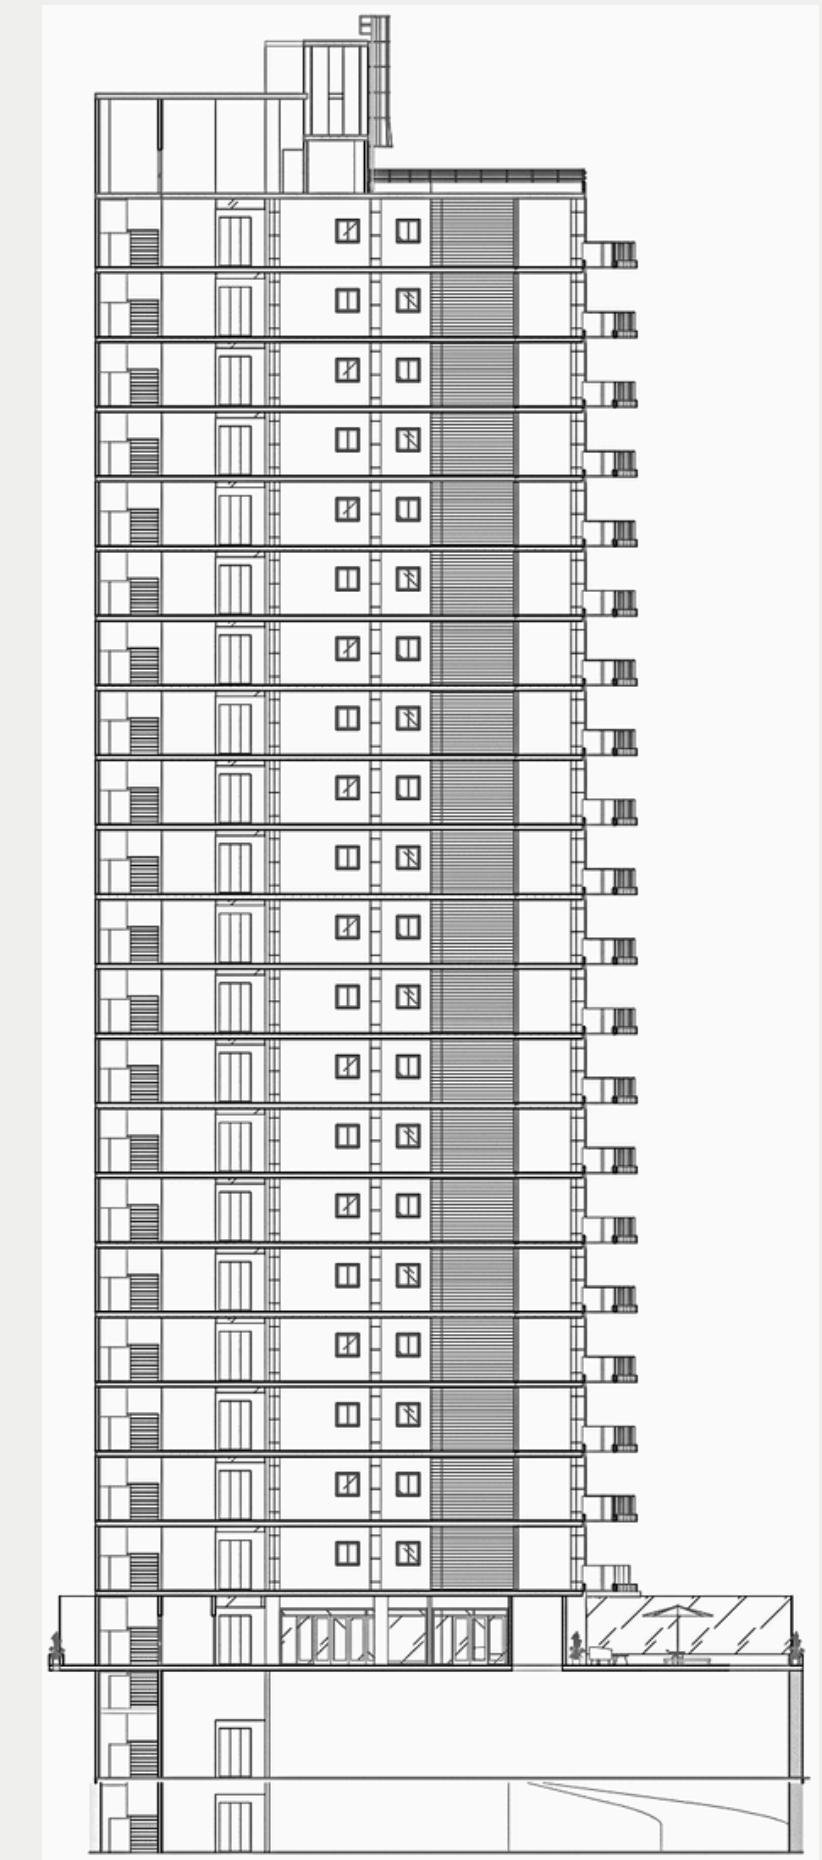

CORTE LONGITUDINAL

# Obrigada!

Entre em contato:

📞 (85) 99760-3925

✉️ deboramariaandrade12@gmail.com

linkedin.com/in/débora-maria-  
75b087347

🌐 @deboramaria\_12

*Portfólio 2025 / Débora Maria*

